
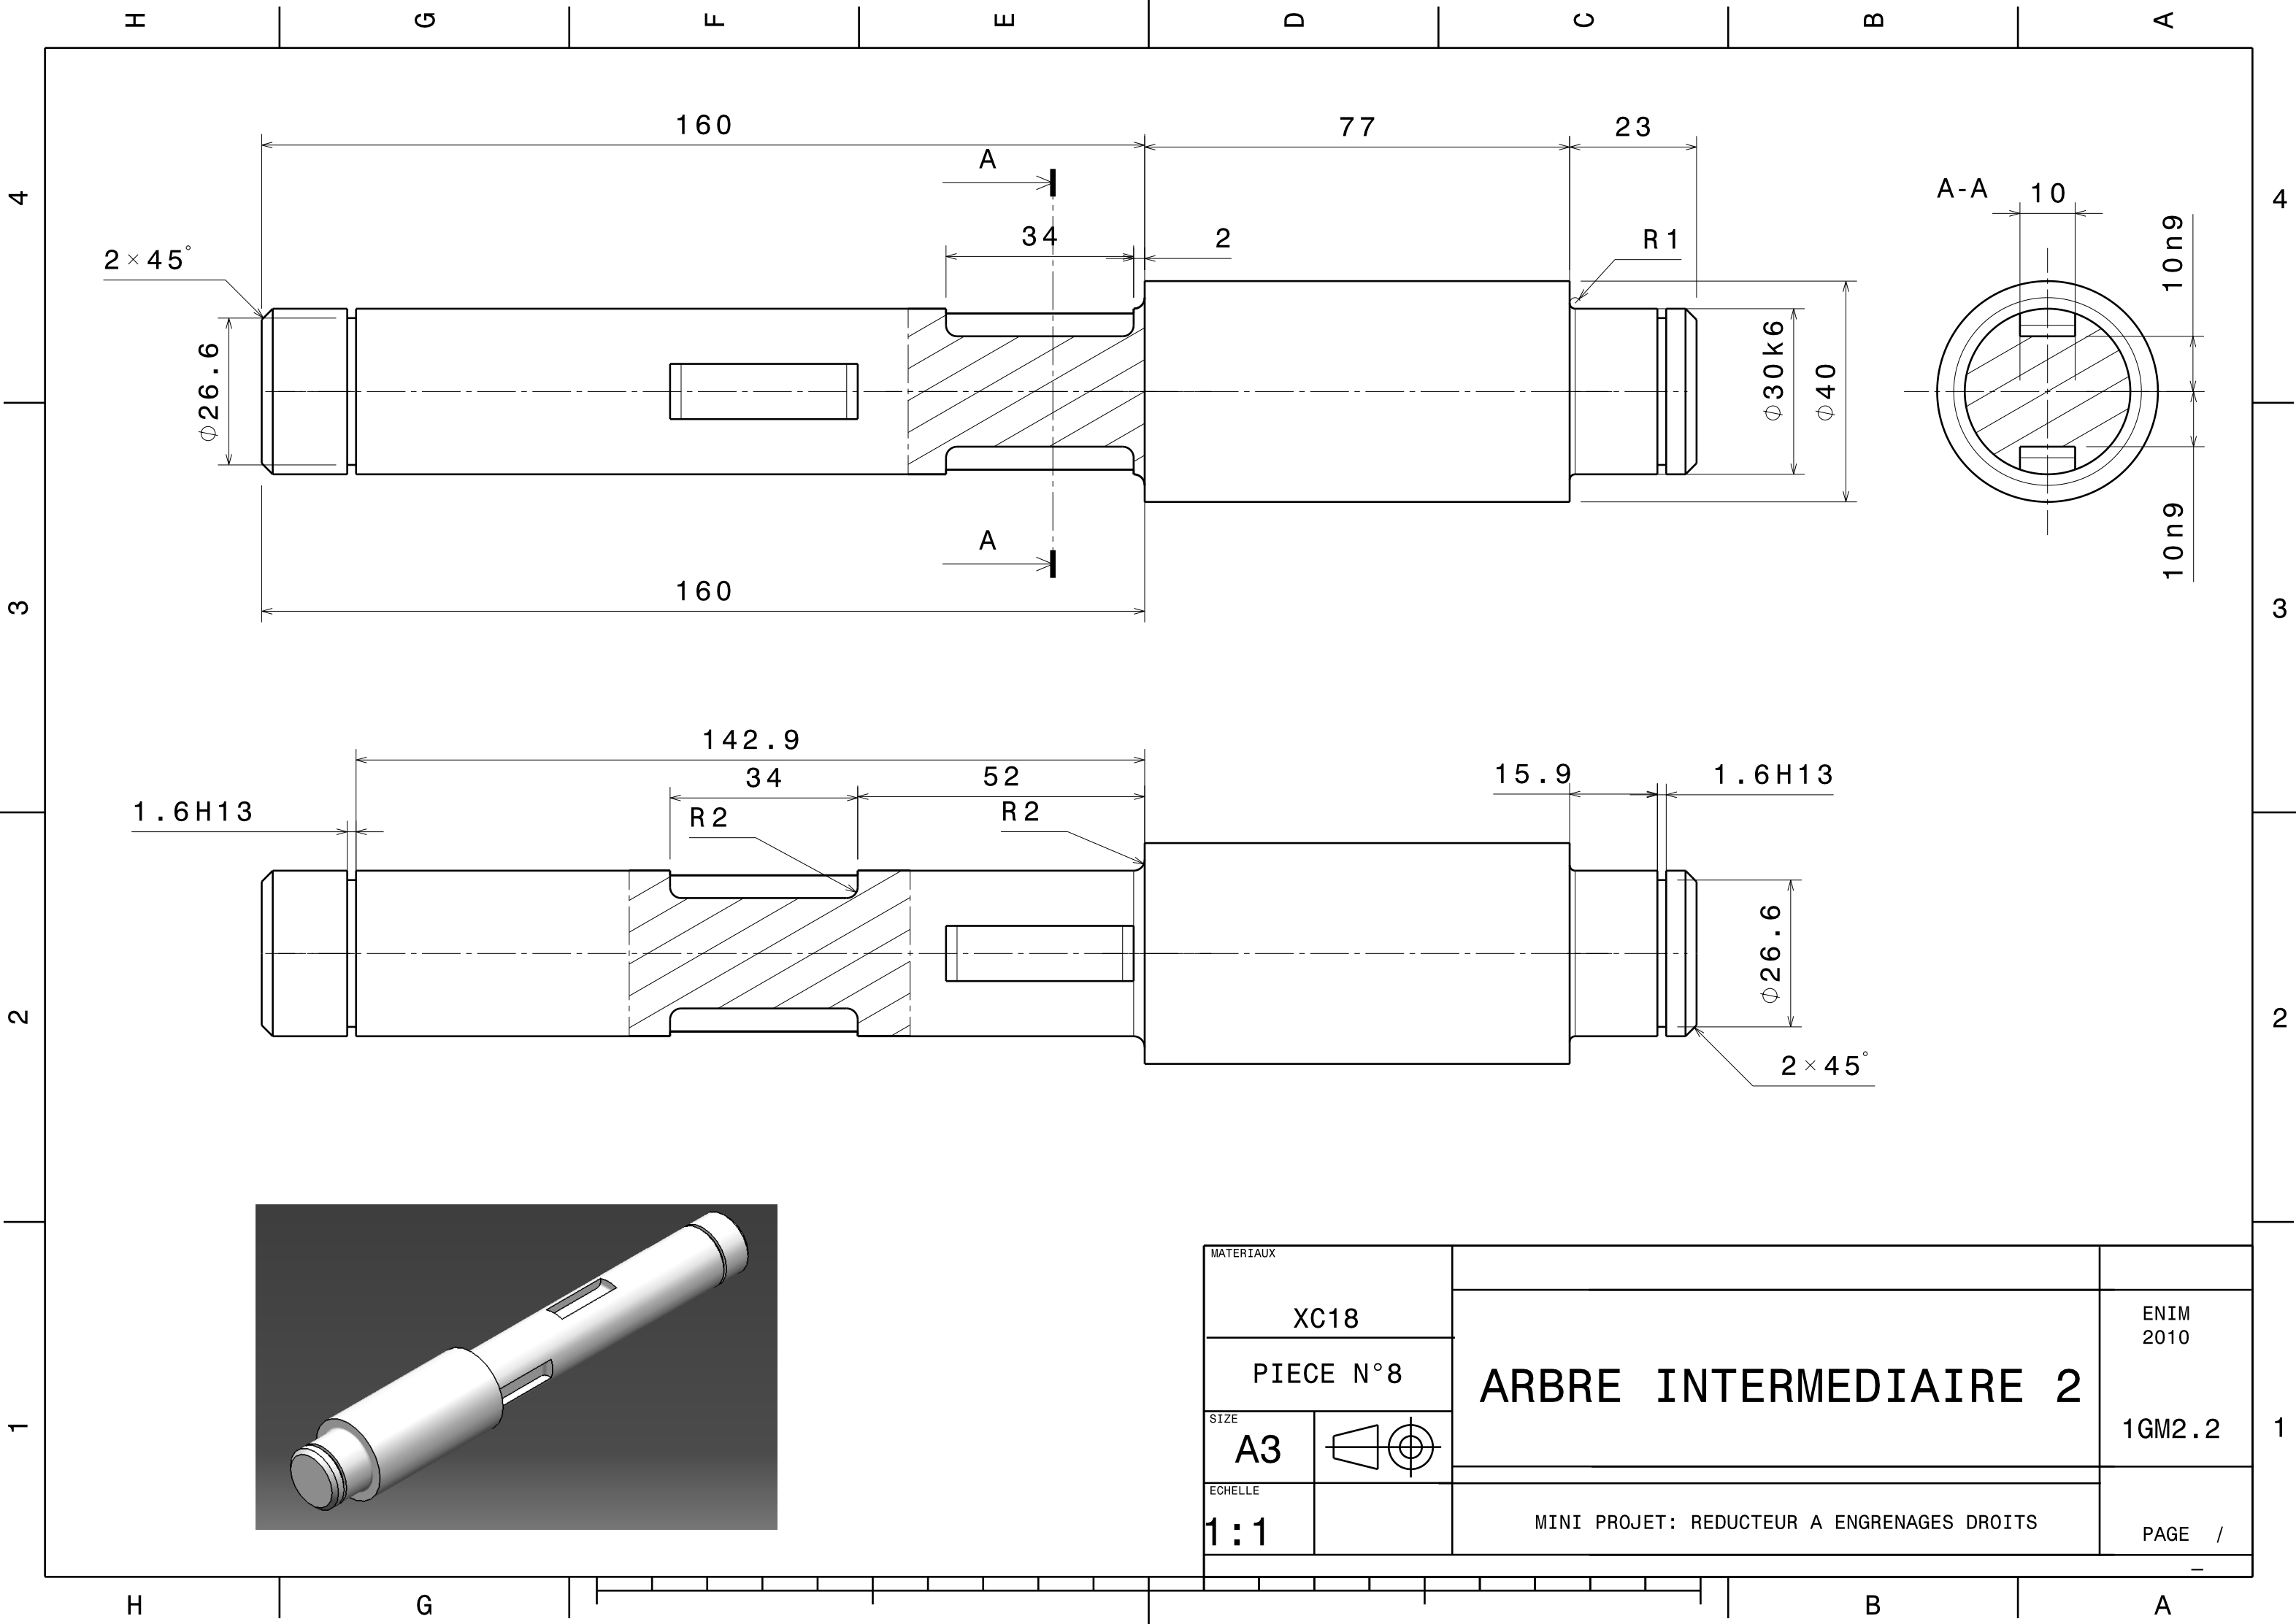


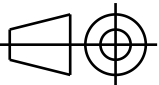

|           |                                                                                       |                                            |              |
|-----------|---------------------------------------------------------------------------------------|--------------------------------------------|--------------|
| MATERIAUX |                                                                                       |                                            |              |
| XC18      |                                                                                       | ARBRE INTERMEDIAIRE 2                      | ENIM<br>2010 |
| PIECE N°8 |                                                                                       |                                            | 1GM2.2       |
| SIZE      |  |                                            |              |
| A3        |                                                                                       |                                            |              |
| ECHELLE   |                                                                                       | MINI PROJET: REDUCTEUR A ENGRENAGES DROITS | PAGE /       |
| 1 : 1     |                                                                                       |                                            |              |